
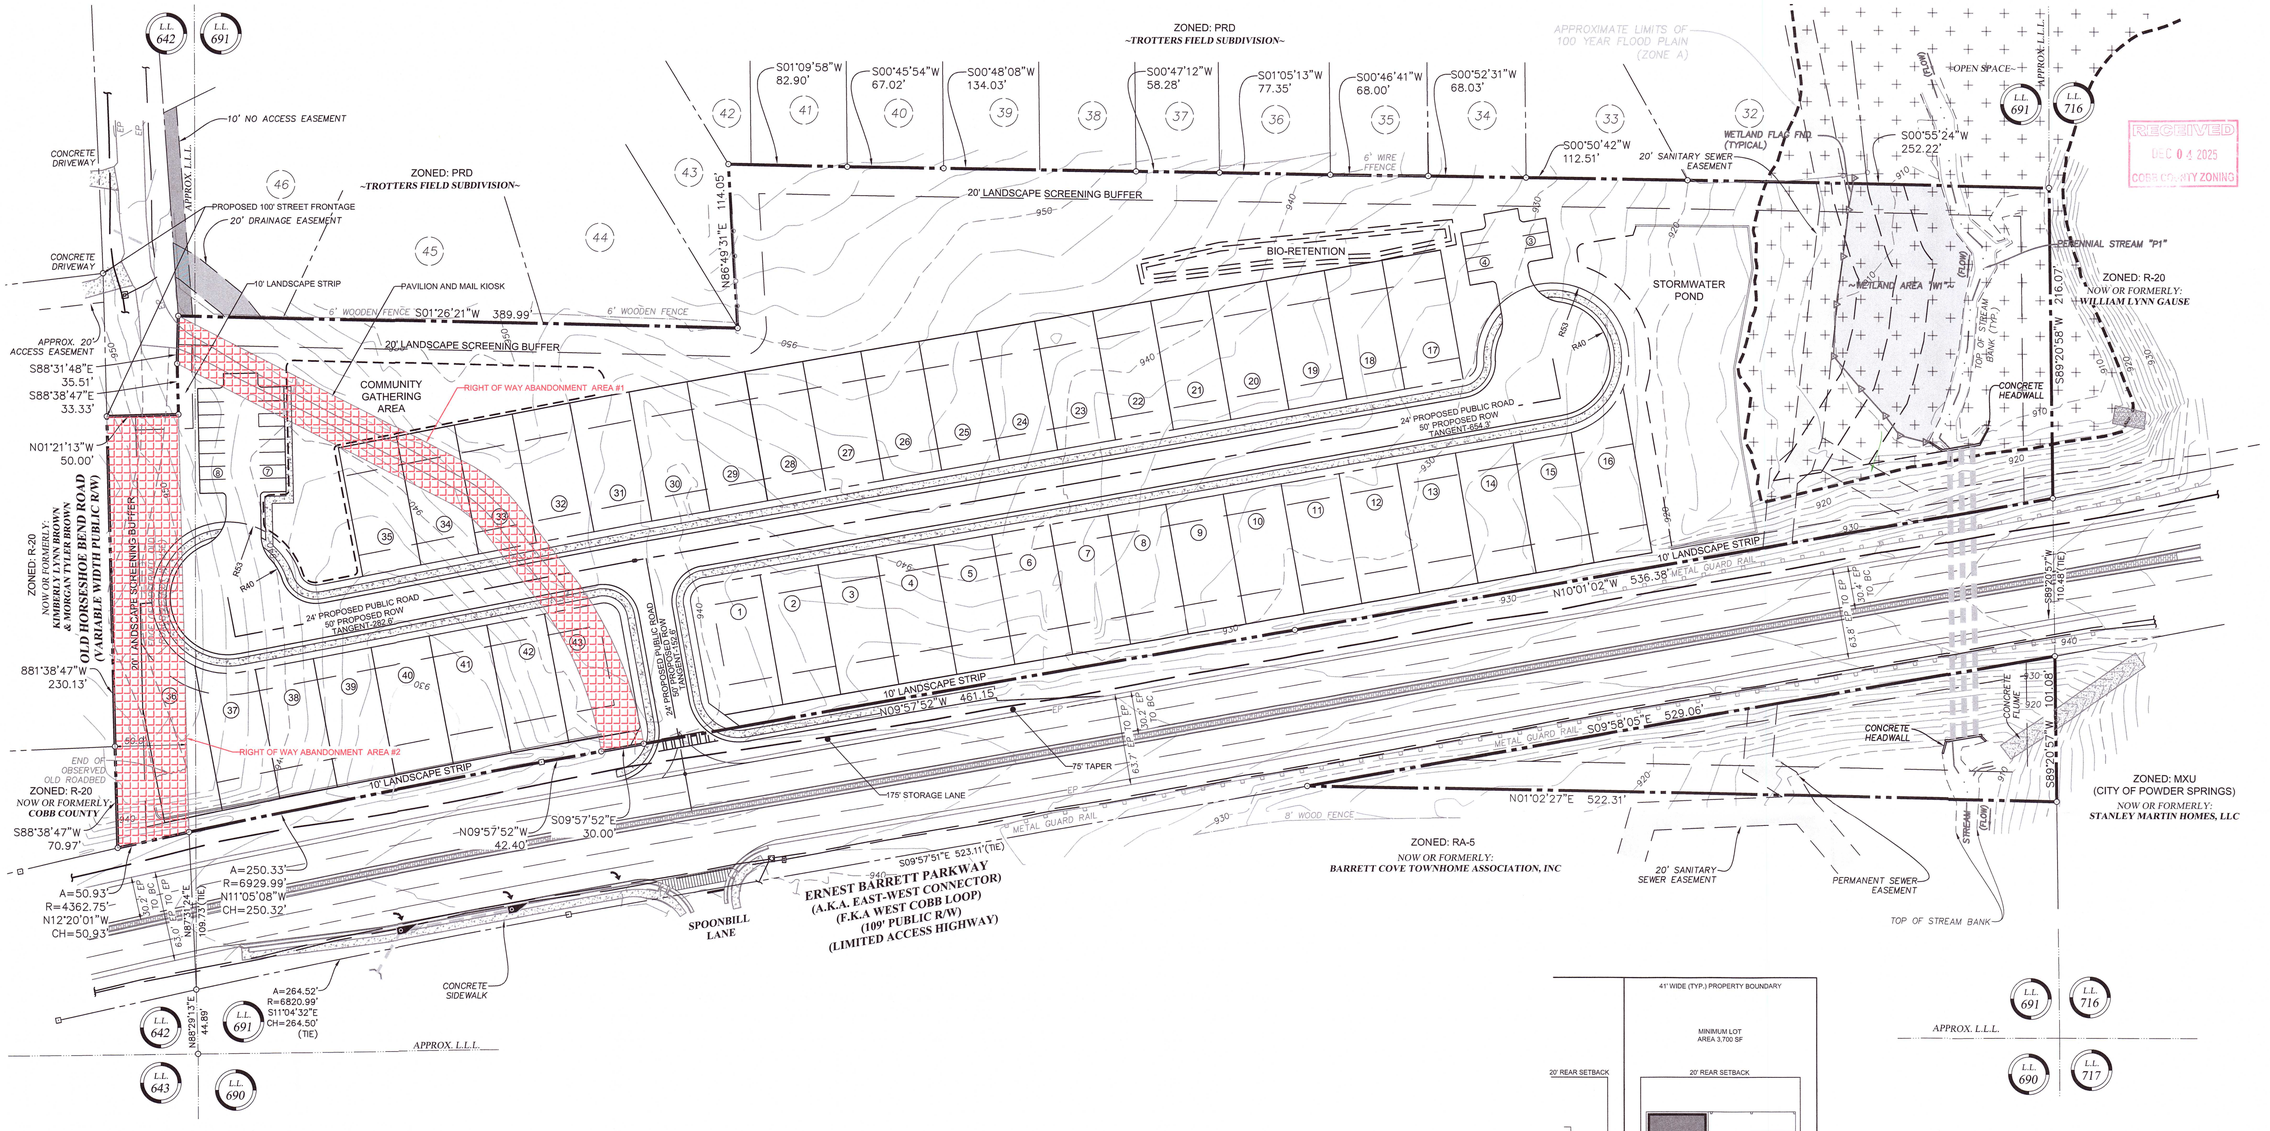


RECEIVED
DEC 04 2025
COBB COUNTY ZONING

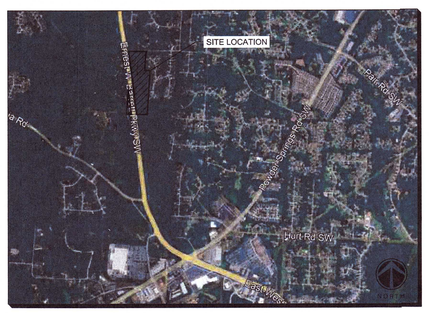

SITE LOCATION MAP
NOT TO SCALE


GEORGIA811
www.Georgia811.com
Know what's below. Call before you dig.

24 HOUR CONTACT:
NEVILLE ALLISON
678-223-8978

GENERAL NOTES:

1. STREAMS AND WETLANDS ARE LOCATED ON THE SITE
2. PROPERTY IS LOCATED WITHIN A SPECIAL FLOOD HAZARD AREA ACCORDING TO FEDERAL EMERGENCY MANAGEMENT AGENCY (FEMA), AS SHOWN ON FLOOD INSURANCE RATE MAP PANEL 0094H, WITH A DATE OF IDENTIFICATION OF MARCH 4, 2013 FOR COMMUNITY NO. 13067C, COBB COUNTY, GEORGIA. WHICH IS THE CURRENT FLOOD INSURANCE RATE MAP FOR THE COMMUNITY IN WHICH SAID PREMISES IS LOCATED
3. POWER AND GAS EASEMENTS ARE LOCATED ON THE SITE IN THE EXISTING RIGHT OF WAY
4. NO CEMETERIES ARE LOCATED ON THE SITE
5. SPEED LIMIT ON EARNEST BARRETT PARKWAY IS 45 MPH
6. WATER UTILITY PROVIDER IS COBB COUNTY
7. SANITARY SEWER PROVIDER IS COBB COUNTY
8. SIZE AND LOCATION OF PROPOSED STRUCTURES AS INDICATED ON SITE PLAN

0 50 100 150 feet
1" = 50'-0"

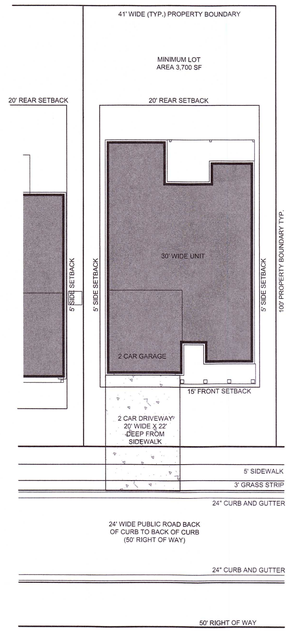

TYPICAL LOT LAYOUT

SITE DATA:	
SITE AREA	10.171 ACRES OR 443,038 SF
FLOOD PLAIN	0.956 ACRES OR 41,645 SF (= 0.478 AC)
NET SITE AREA	9.693 ACRES OF 422,216 SF
ZONING	
EXISTING ZONING	R-20
PROPOSED ZONING	RA-5
LOT DIMENSIONS	
MINIMUM LOT AREA	7,000 SF (PROPOSED 3,700 SF)
MIN./MAX. ACERAGE REQUIRED	80,000 SF/20 ACRES
MAXIMUM DENSITY	5 UNITS PER ACRE
MINIMUM FLOOR AREA	950 SF
MINIMUM LOT WIDTH AT FRONT SETBACK	70 FEET/50 FEET (PROPOSED 41 FEET)
BUILDING SETBACKS	
FRONT YARD SETBACK ARTERIAL STREET	50 FEET (N/A)
FRONT YARD SETBACK INTERIOR STREET	20 FEET (PROPOSED 15 FEET)
MAJOR SIDE YARD SETBACK	20 FEET (PROPOSED 15 FEET)
SIDE SETBACK INTERIOR	5 FEET
REAR SETBACK ARTERIAL STREET	40 FEET (PROPOSED 30 FEET)
REAR SETBACK INTERIOR	30 FEET (PROPOSED 20 FEET)
DEVELOPMENT STANDARDS	
MINIMUM FLOOR AREA	950 SF
BUILDING HEIGHT	35 FEET
MAXIMUM COVERAGE	40% OR 1,295 SF (PROPOSED 45% OR 1,650 SF)
MAXIMUM IMPERVIOUS AREA	35% OR 155,063 SF
PROPOSED UNITS	43 UNITS
PROPOSED DENSITY	4.44 UNITS PER ACRE
GUEST PARKING SPACES (0.5 SPACES PER UNIT)	22 SPACES OR 0.51 SPACES PER UNIT

ENGINEER
THE REVIVE LAND GROUP
SOURCE. ENTITLE. REVIVE.
ONE ALLIANCE CENTER
3500 LENOX ROAD
SUITE 625
ATLANTA, GEORGIA 30326
O: (678) 223-8978
WWW.THEREVIVELANDGROUP.COM

PROJECT
SOMERSET AT MACEDONIA
A MASTER PLANNED RESIDENTIAL DEVELOPMENT

OLD HORSESHOE BEND ROAD AND BARRETT PARKWAY
MARIETTA, GEORGIA 30064

COBB COUNTY
GEORGIA

LAND LOT: 691
DISTRICT: 19TH

CLIENT
THE REVIVE LAND GROUP
SOURCE. ENTITLE. REVIVE.
ONE ALLIANCE CENTER
3500 LENOX ROAD
SUITE 625
ATLANTA, GEORGIA 30326
O: (678) 223-8978
THEREVIVELANDGROUP.COM

REVISION

REVISION	DATE

PROJECT NUMBER
25021

SEAL
GEORGIA REGISTERED PROFESSIONAL ENGINEER CHARLES BARRY ETHRIDGE
PRELIMINARY
NOT TO BE RELEASED FOR CONSTRUCTION
SEAL IS ONLY VALID IF COUNTER SIGNED AND DATED WITH AN ORIGINAL SIGNATURE

NORTH
NORTH

DATE
NOVEMBER 20, 2025

TITLE
CONCEPTUAL SITE PLAN

SHEET
Z-01